


# 1.Propuesta Arquitectonica.

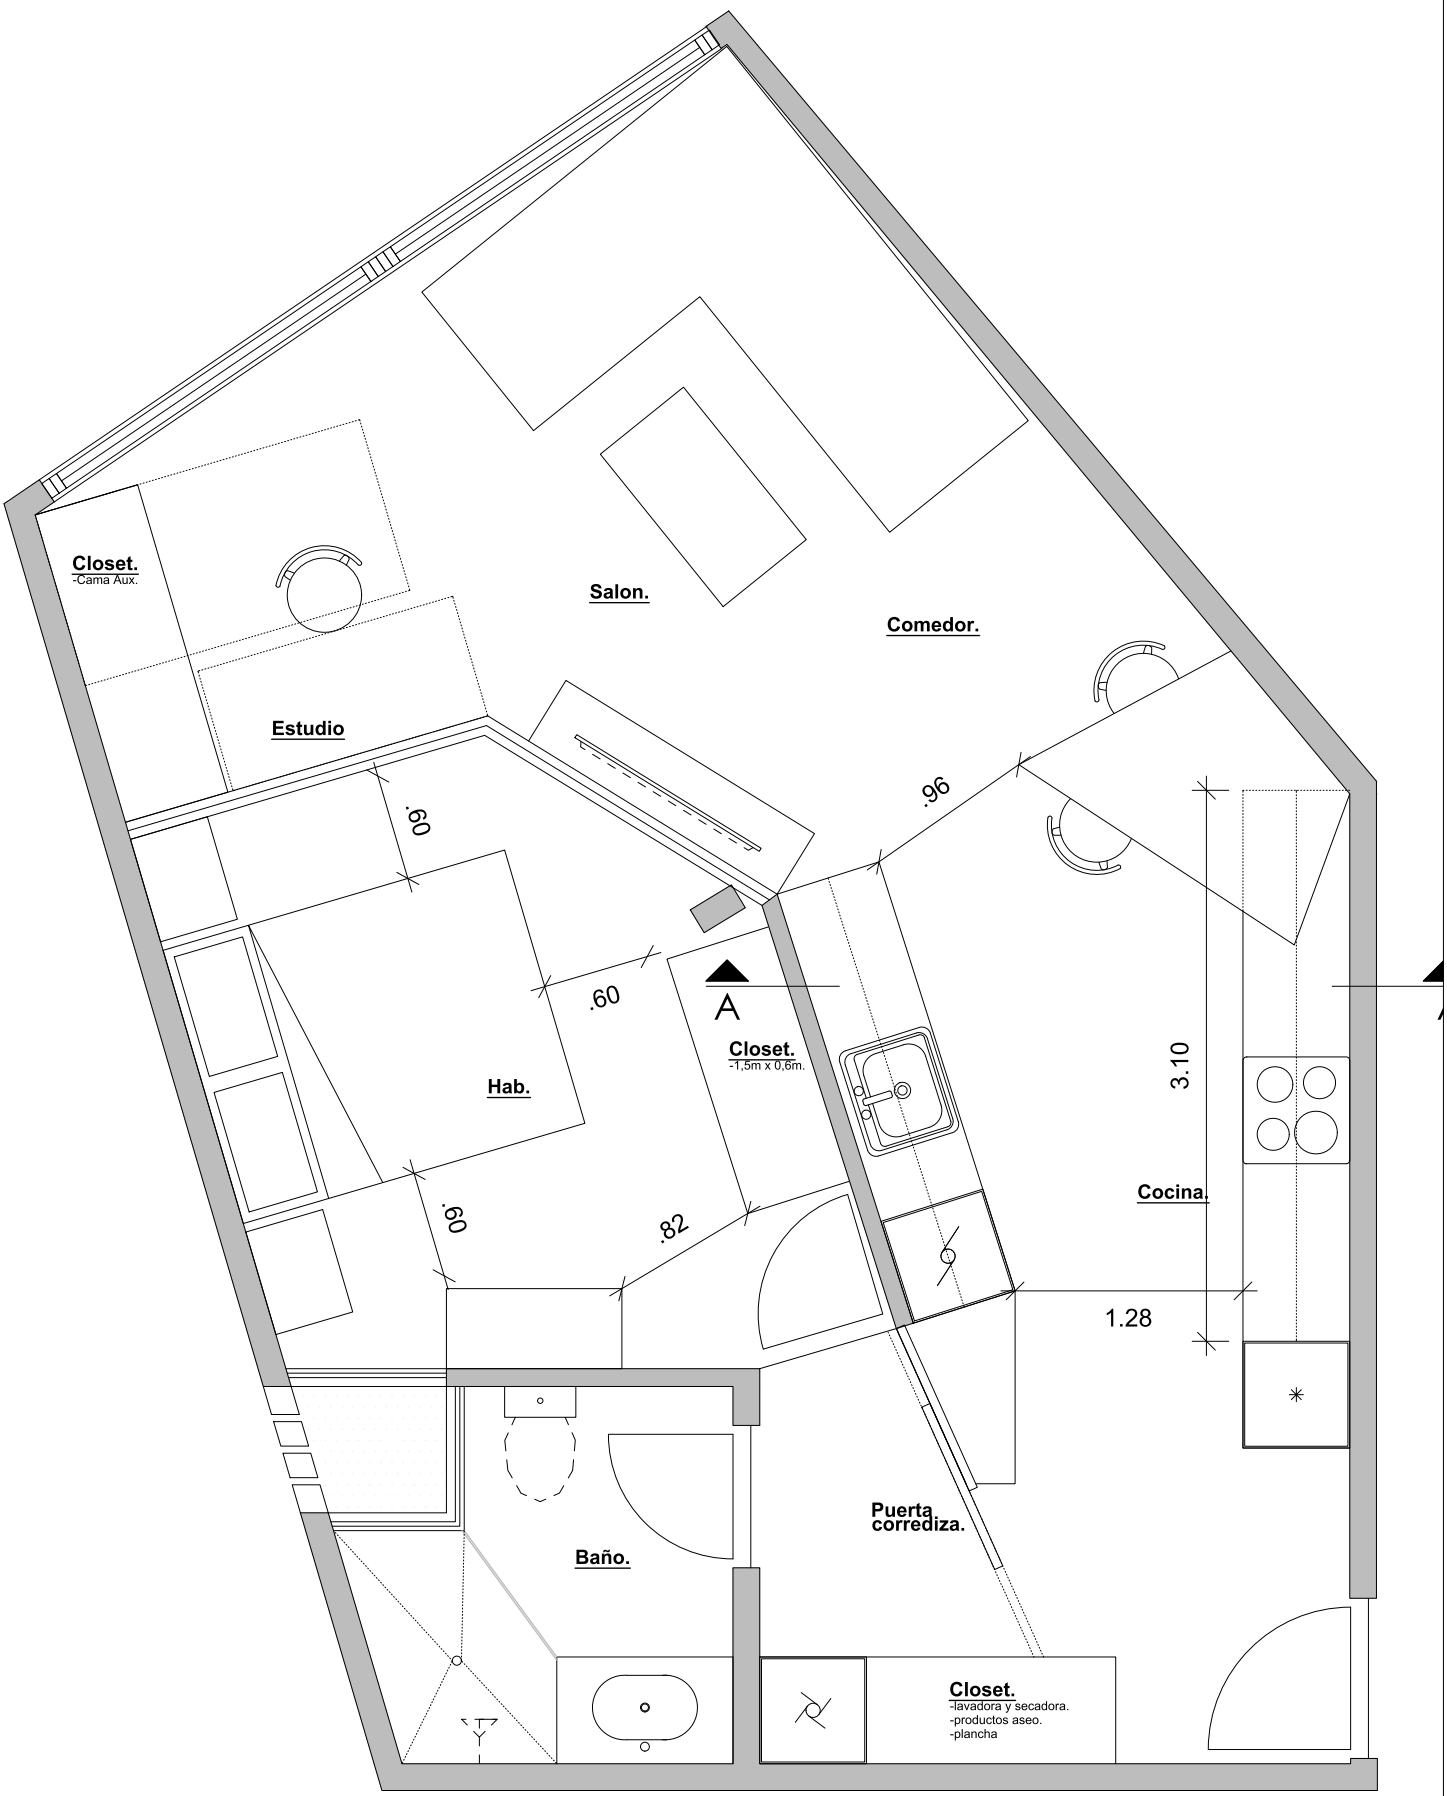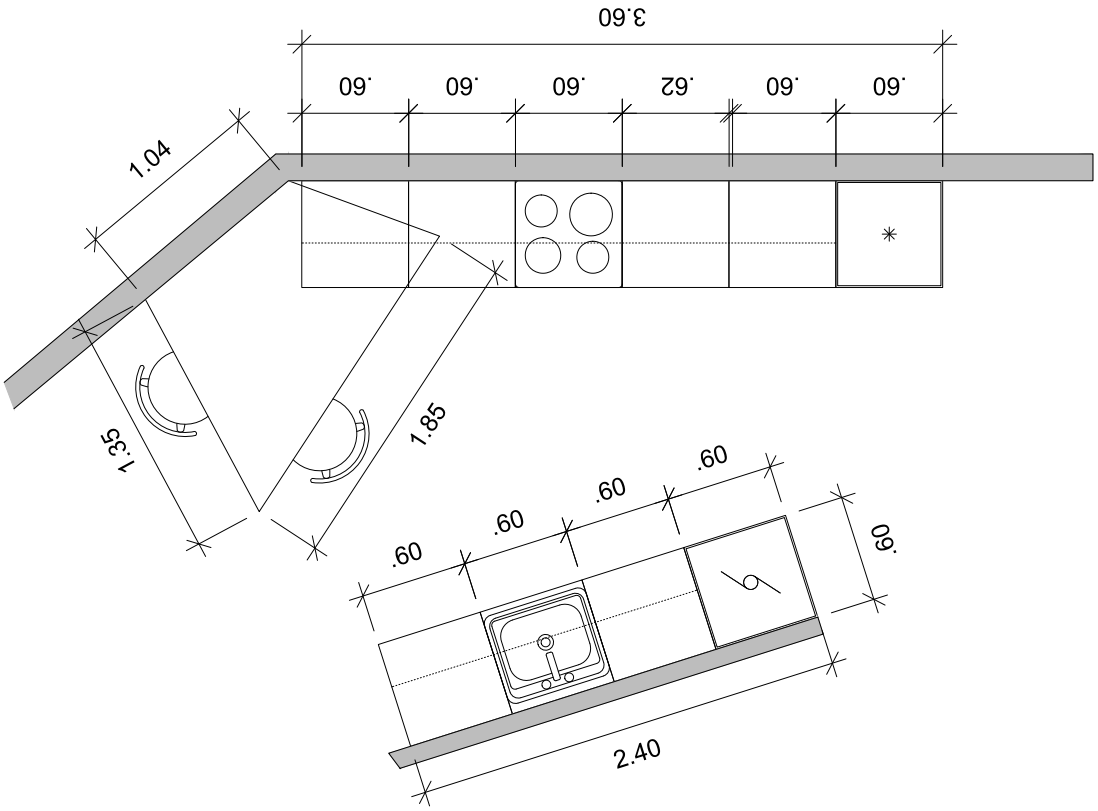


Valencia 178
Escala 1:30

# 2.Detalles Cocina

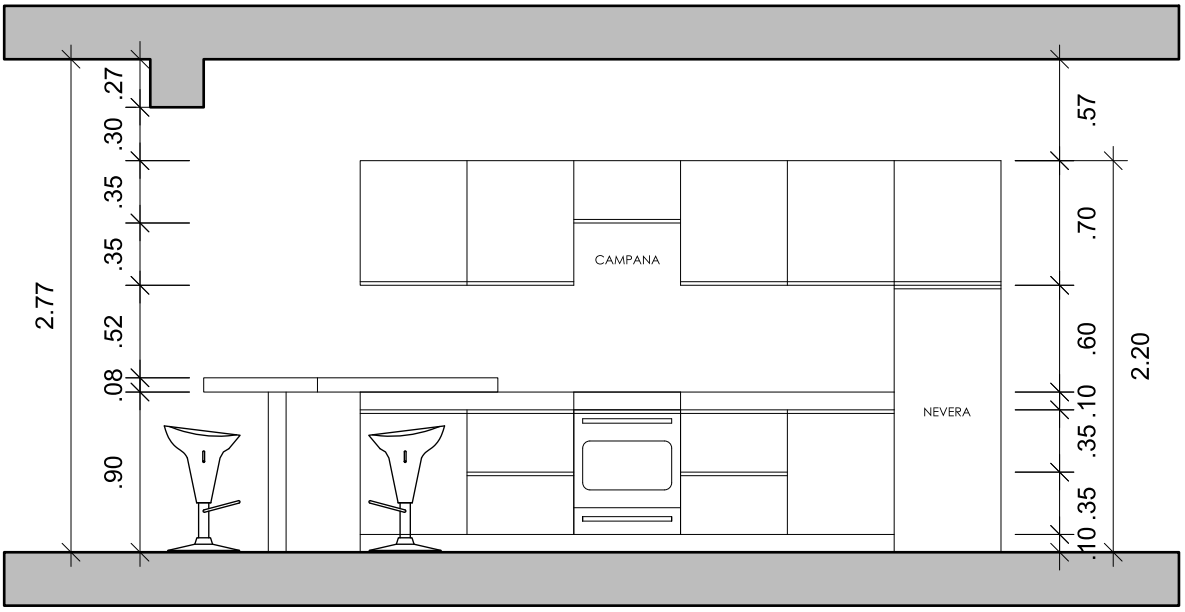




Valencia 178
Escala 1:30

ALZADO COCINA 1

# 2.1.Detalles Cocina

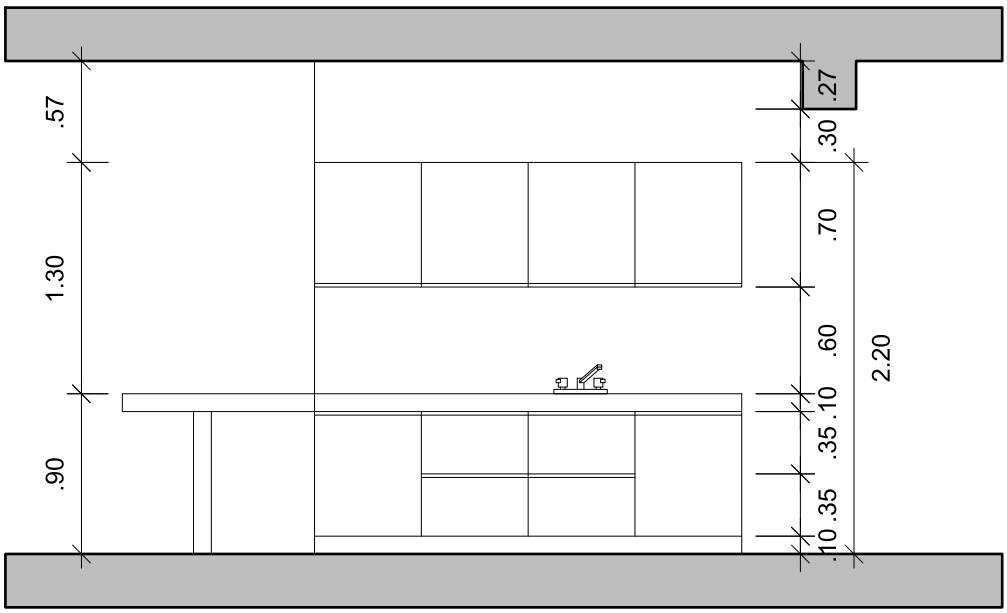



ALZADO COCINA 2

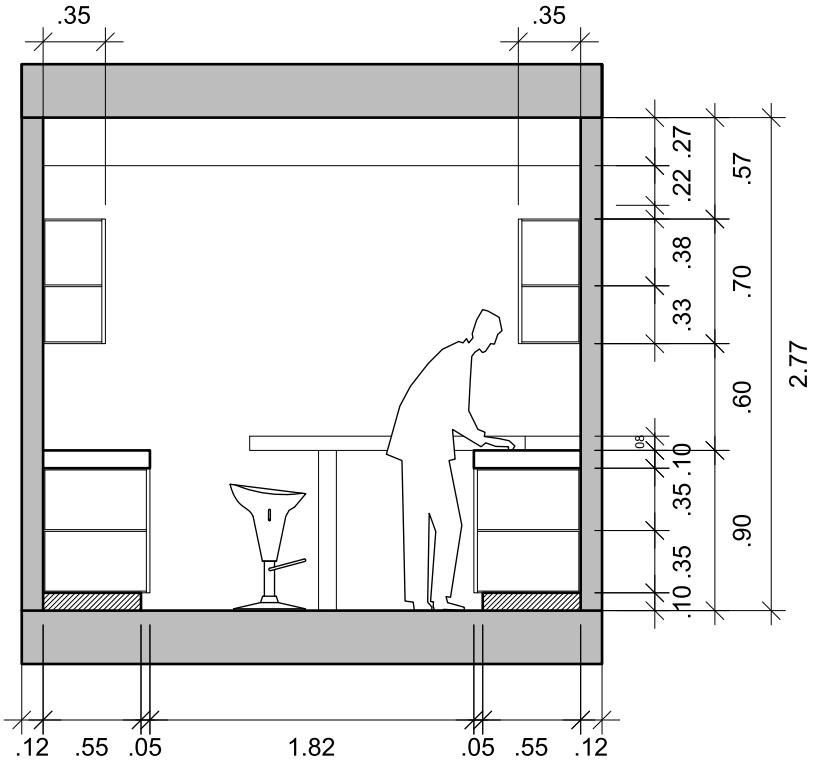



SECCIÓN A-A'

Valencia 178
Escala 1:30

# 3.Despiece pared Metalica.

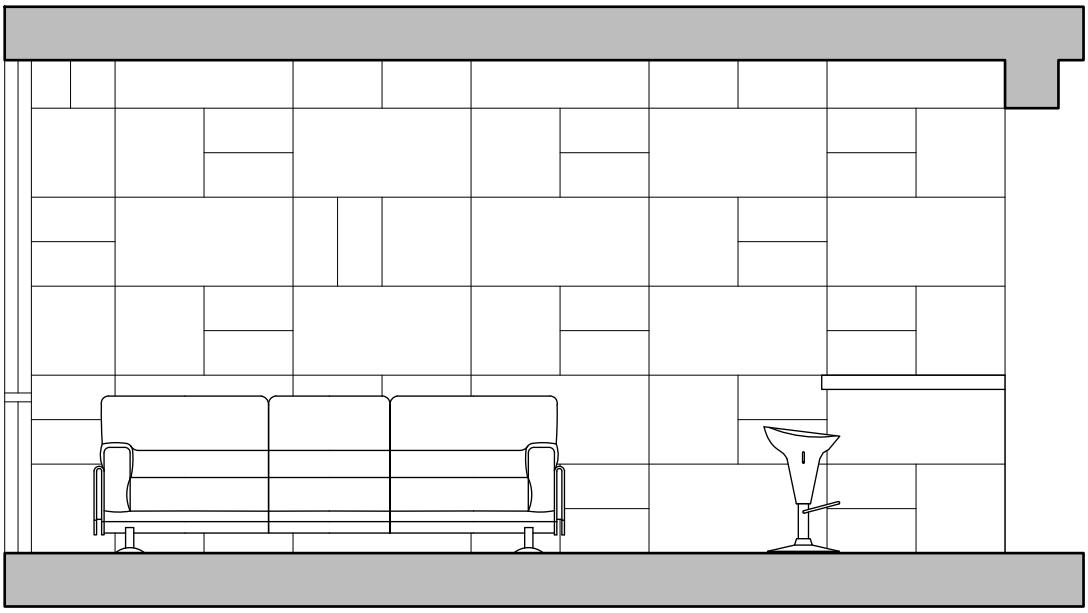

ALZADO MURO METÁLICO

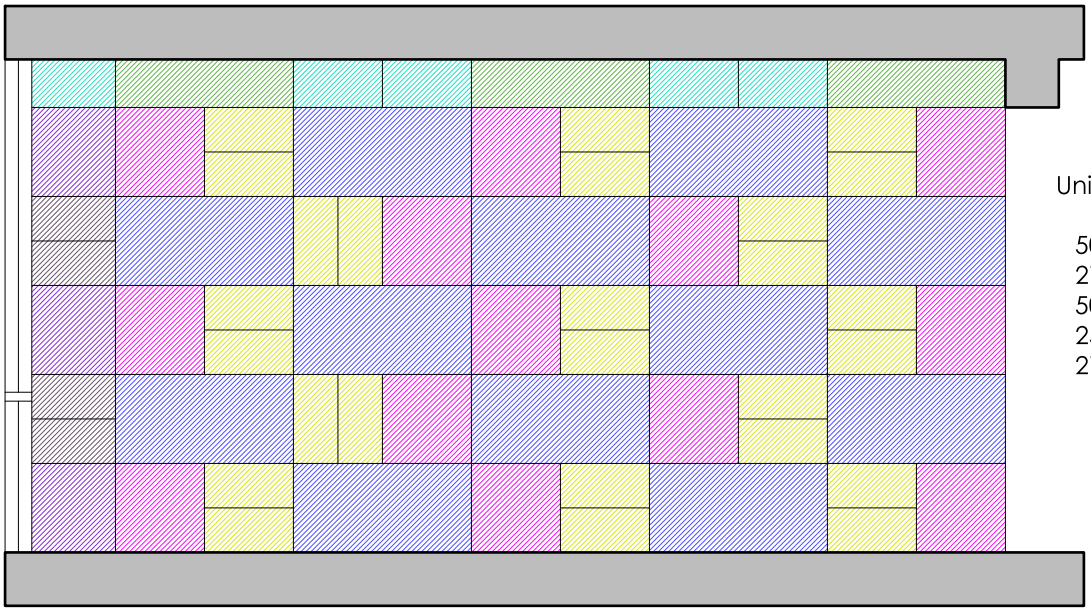


Unidades:

| | |
|---|---|
| 50 x 100 | = 12 und. |
| 27 x 100 | = 3 und. |
| 50 x 50 | = 16 und. |
| 25 x 50 | = 30 und. |
| 27 x 50 | = 5 und. |

Valencia 178
Escala 1:30


DESPIECE MURO METÁLICO

# 4. Red Electrica

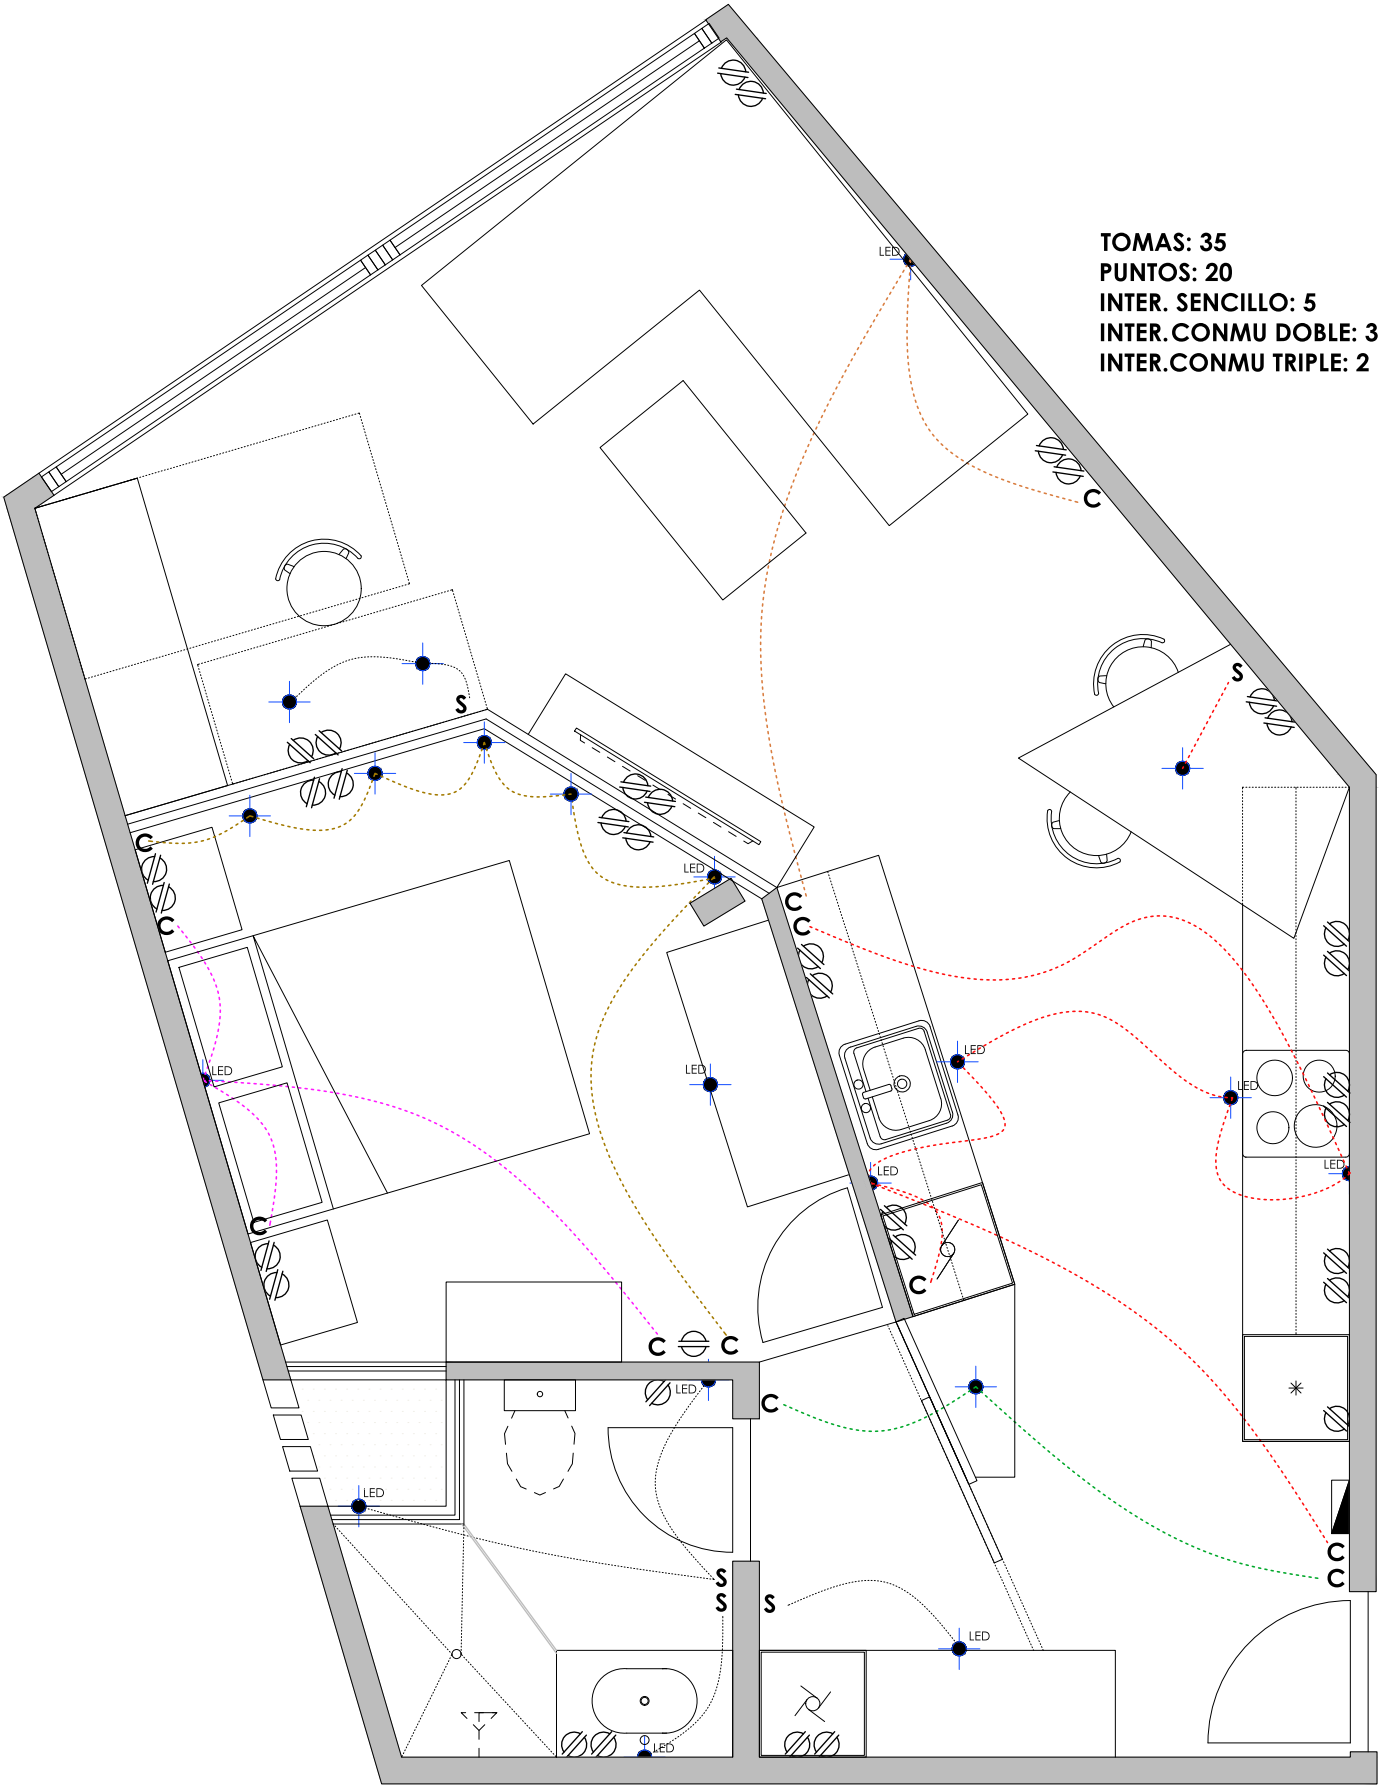



Valencia 178
Escala 1:30

# 5. Red Hidraulica

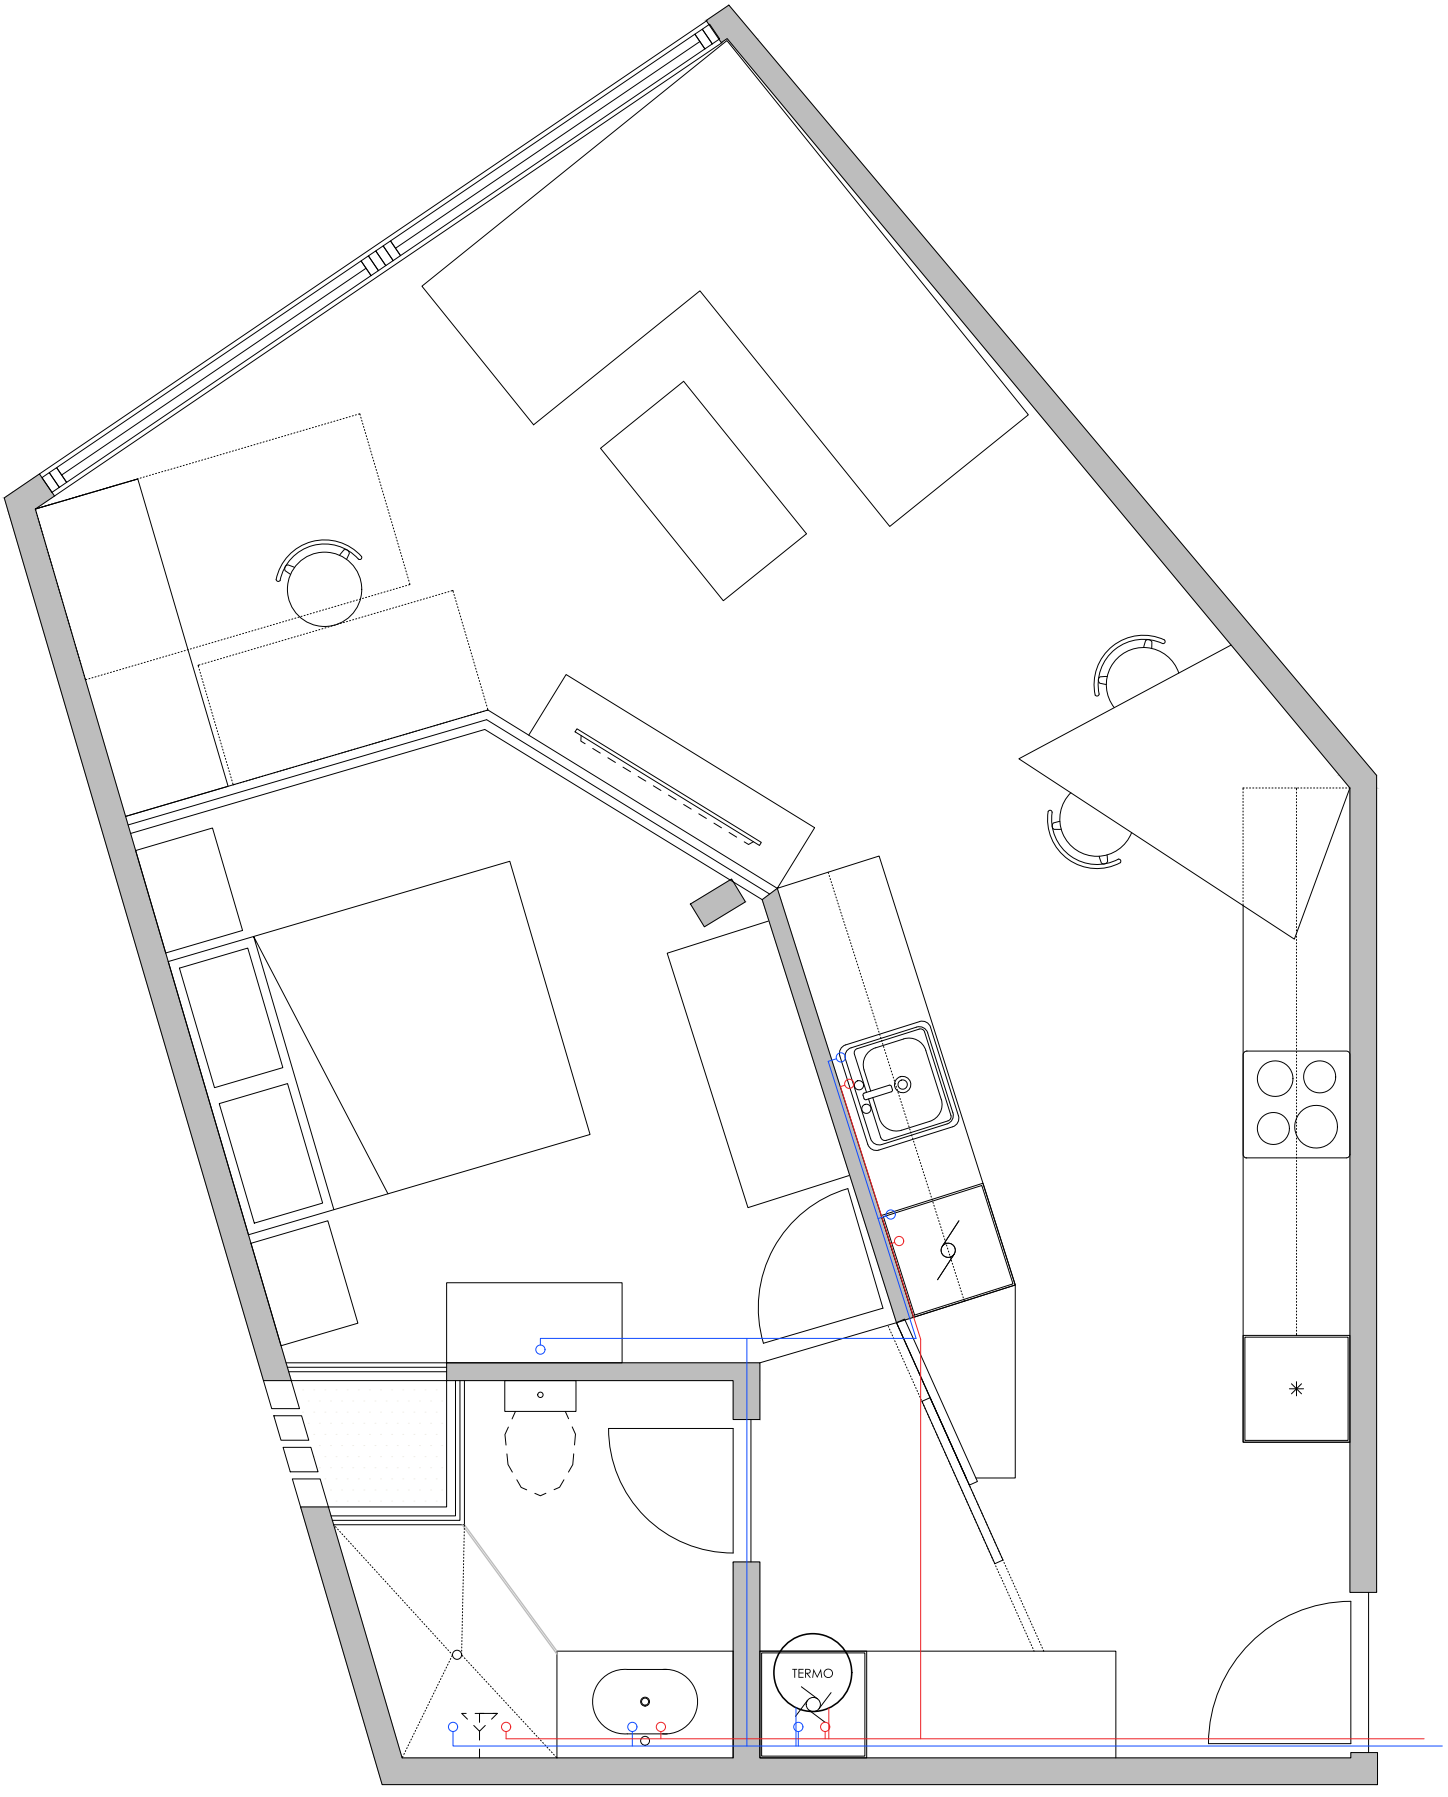



Valencia 178
Escala 1:30

# 6. Red Sanitaria

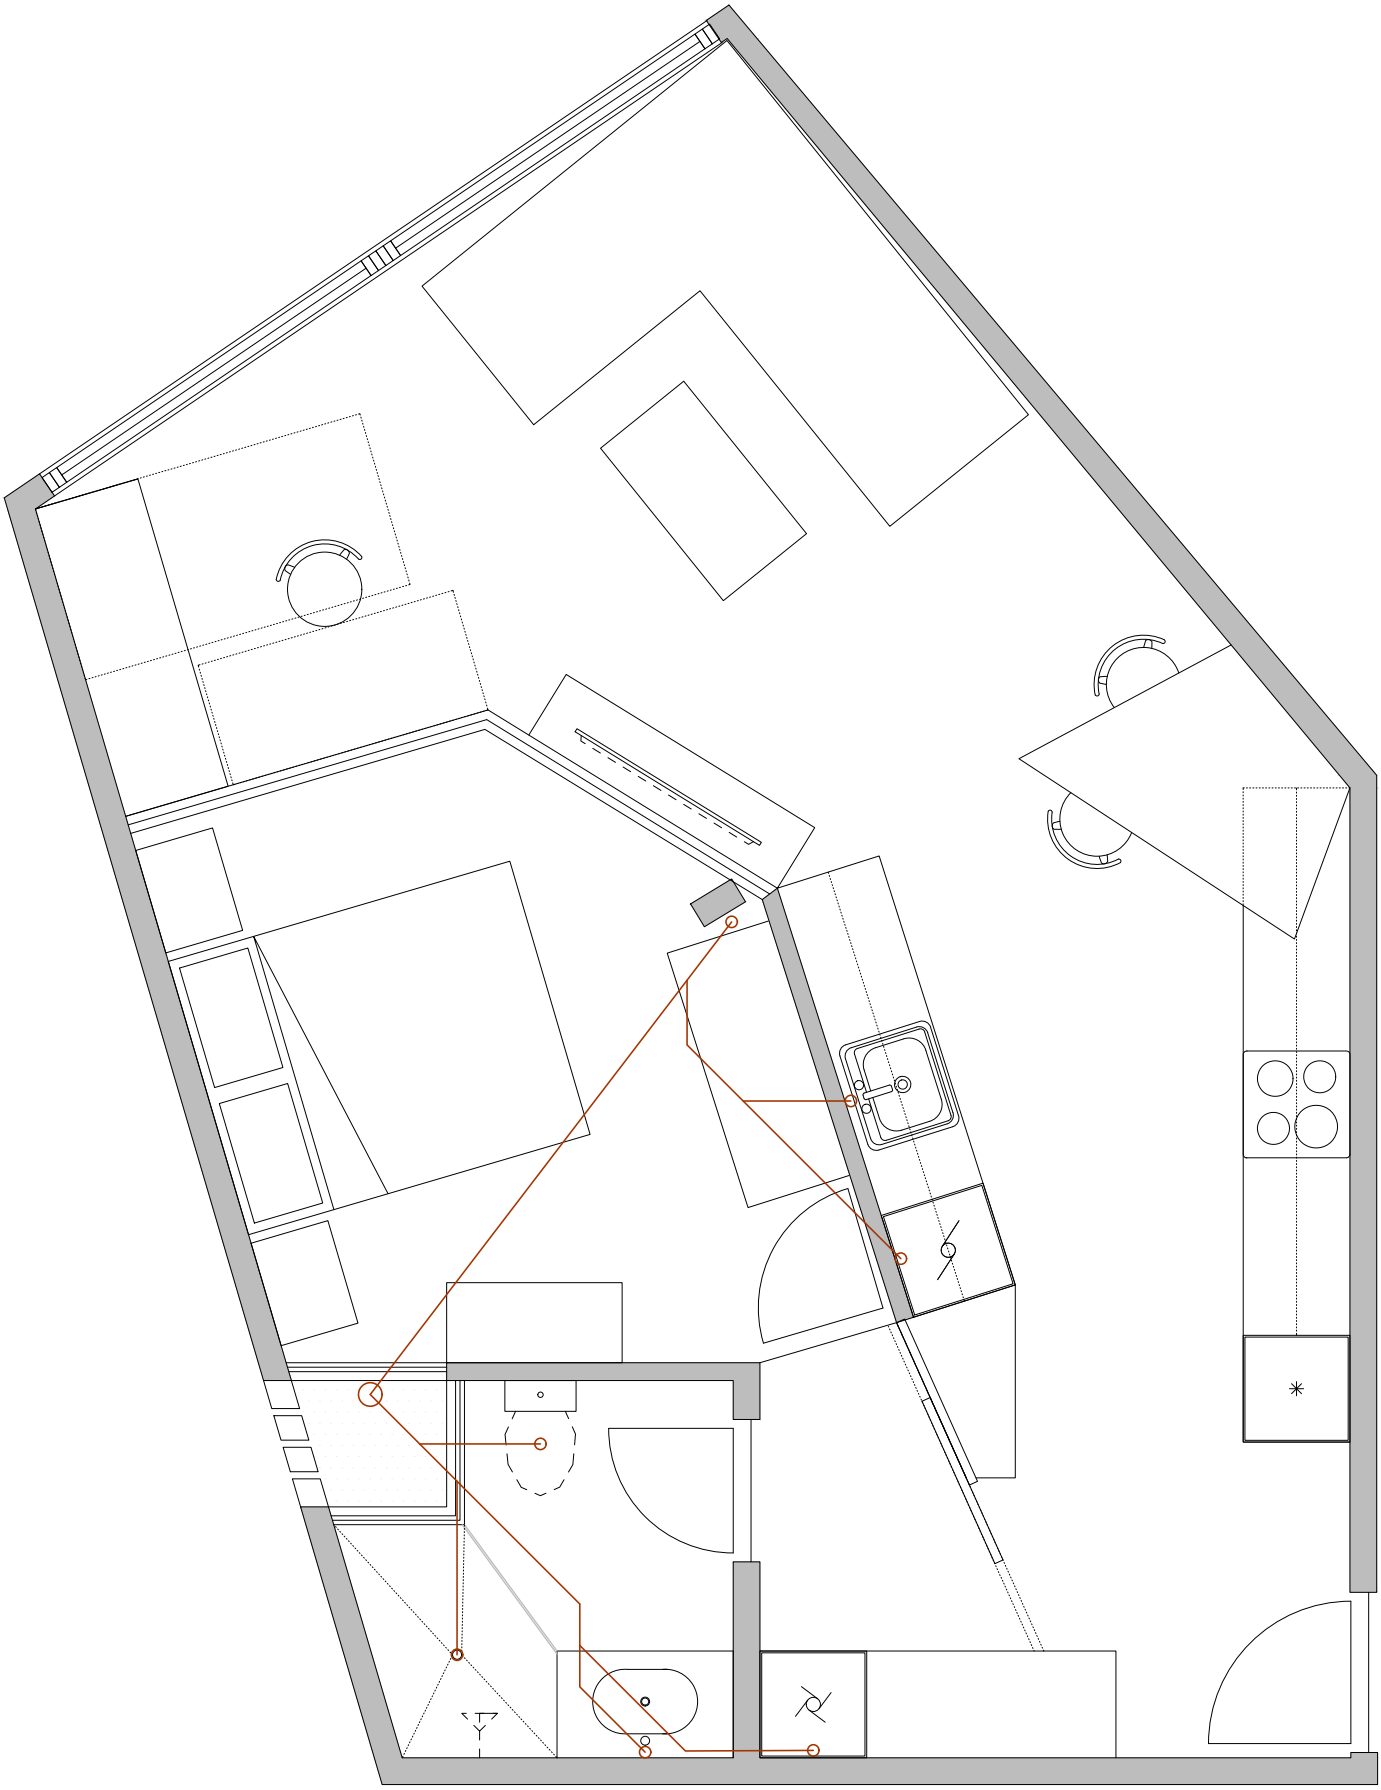


Valencia 178
Escala 1:30

# 7. Extraccion de Humos

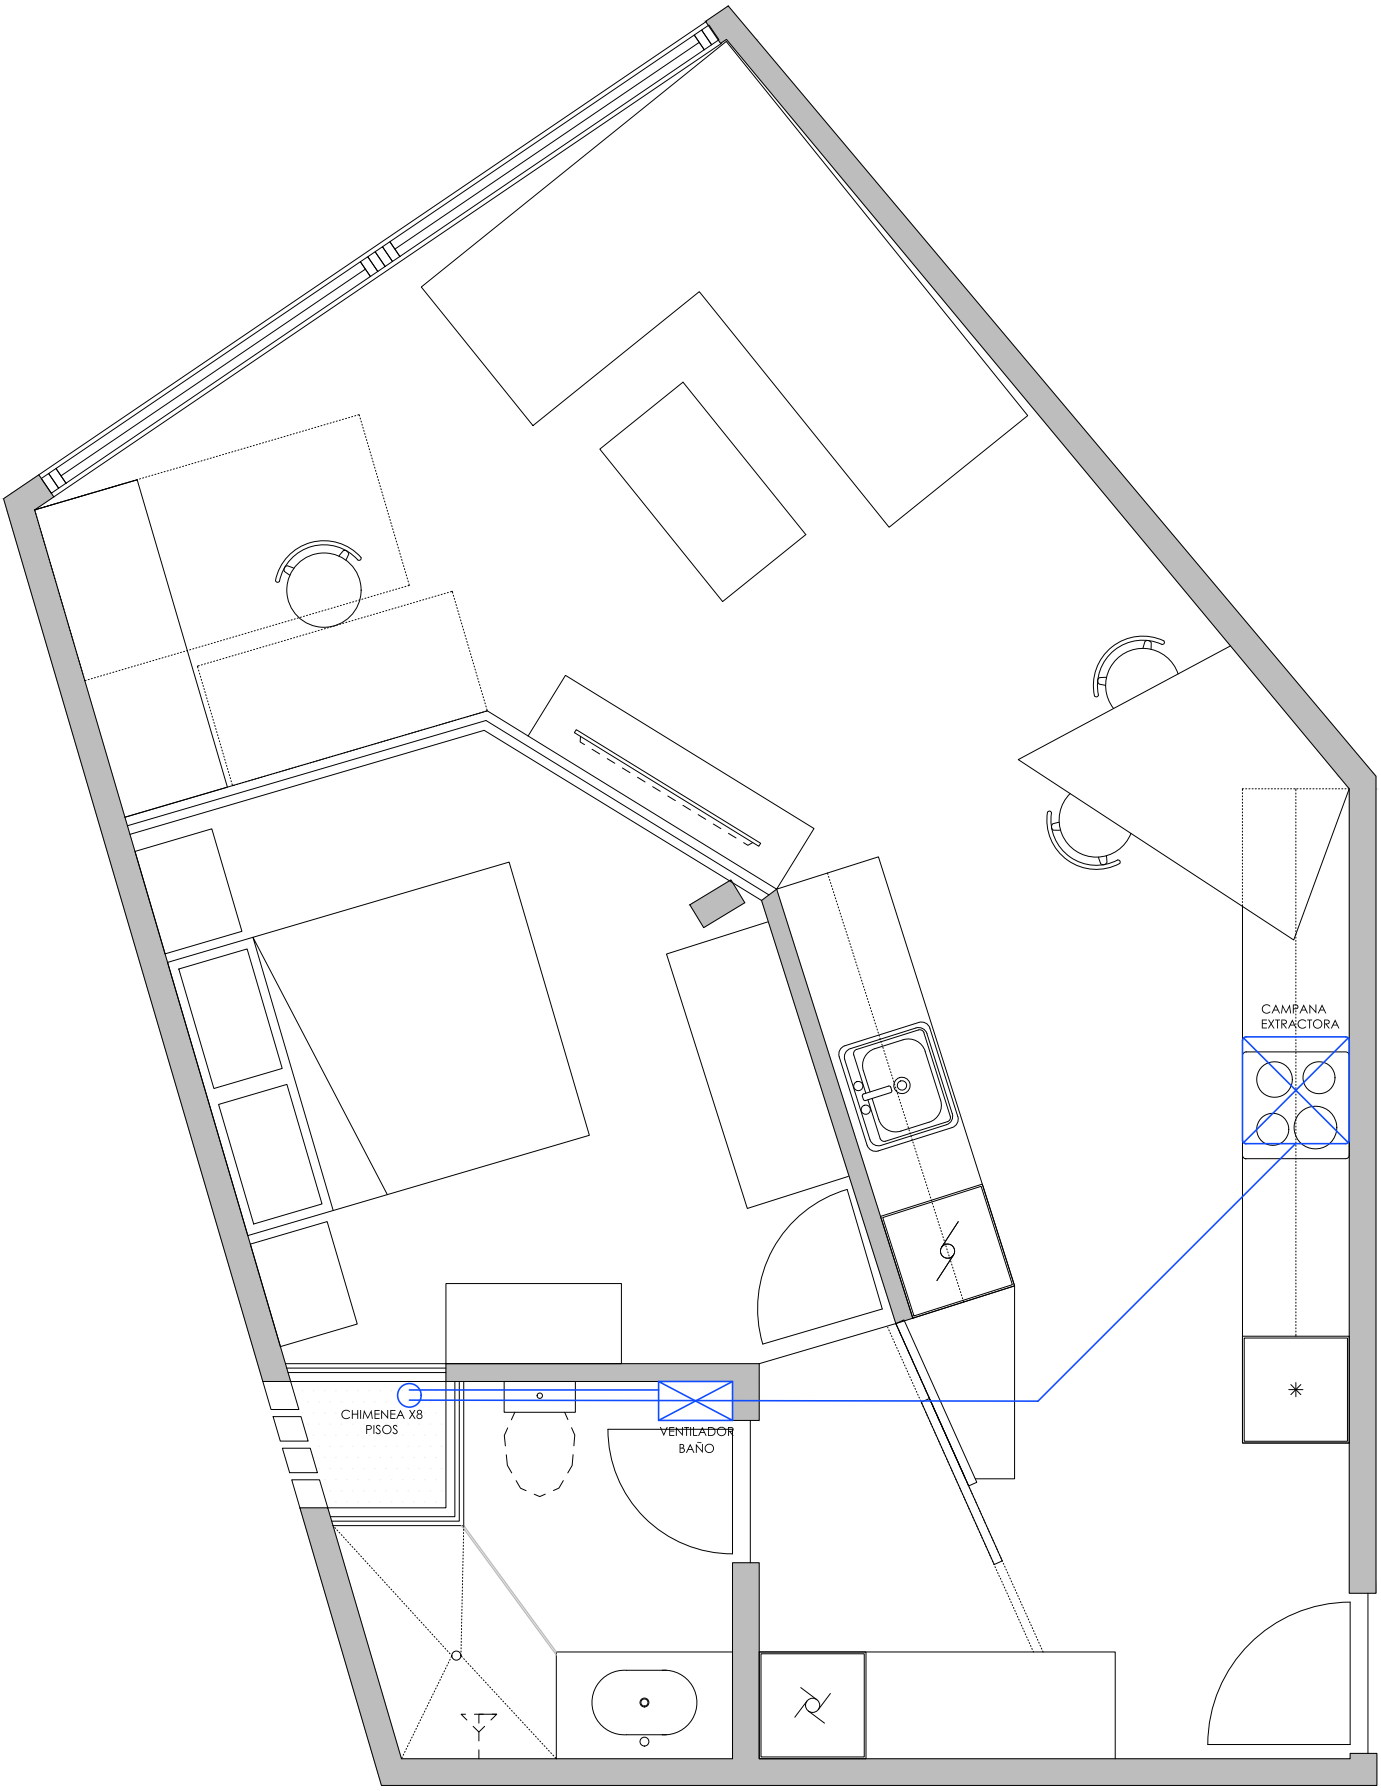



Valencia 178
Escala 1:30

# 8. Aire acondicionado y Clefaccion

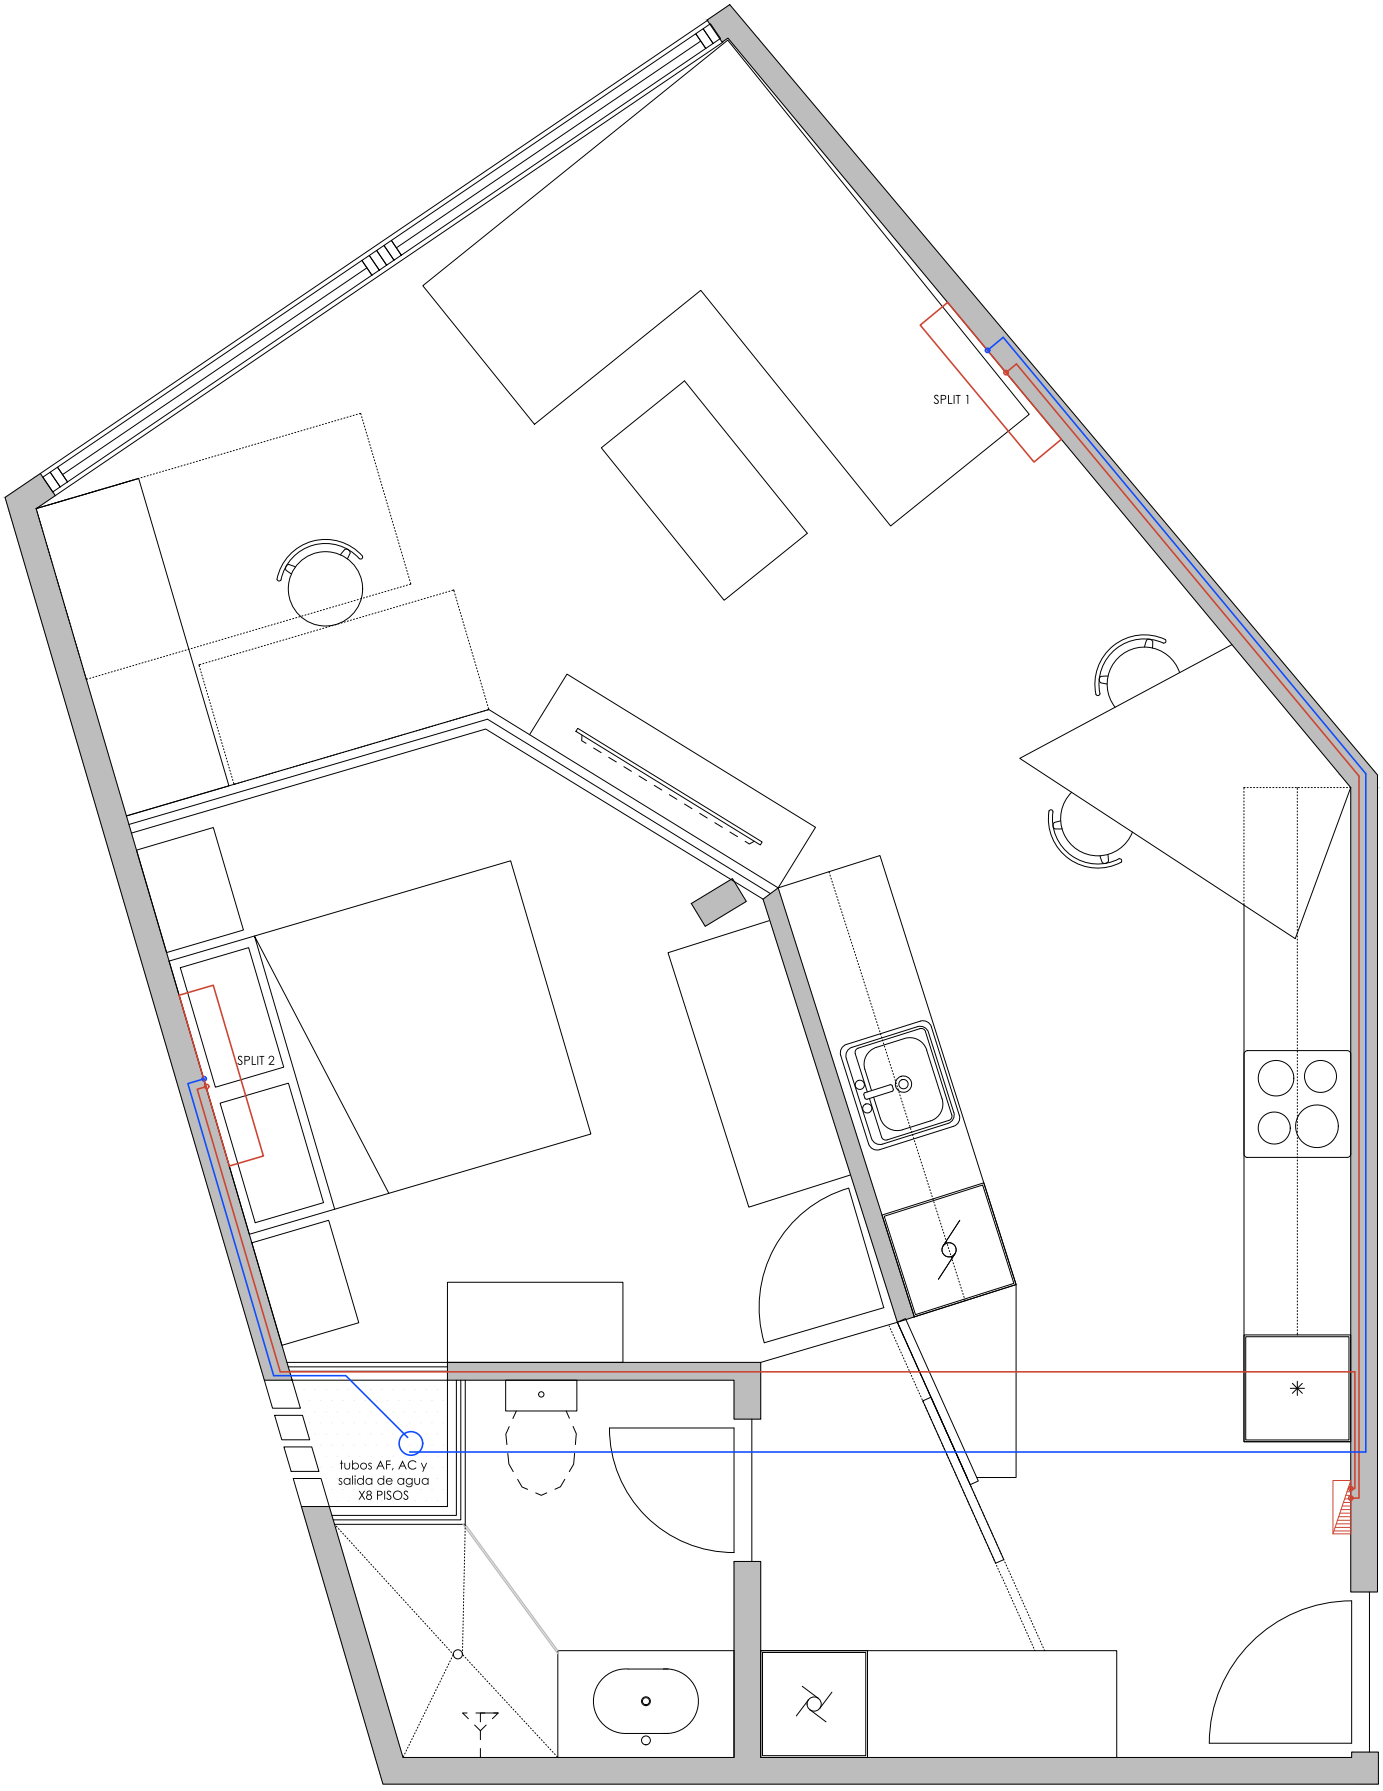


Valencia 178
Escala 1:30

# 9. Techo en pladur

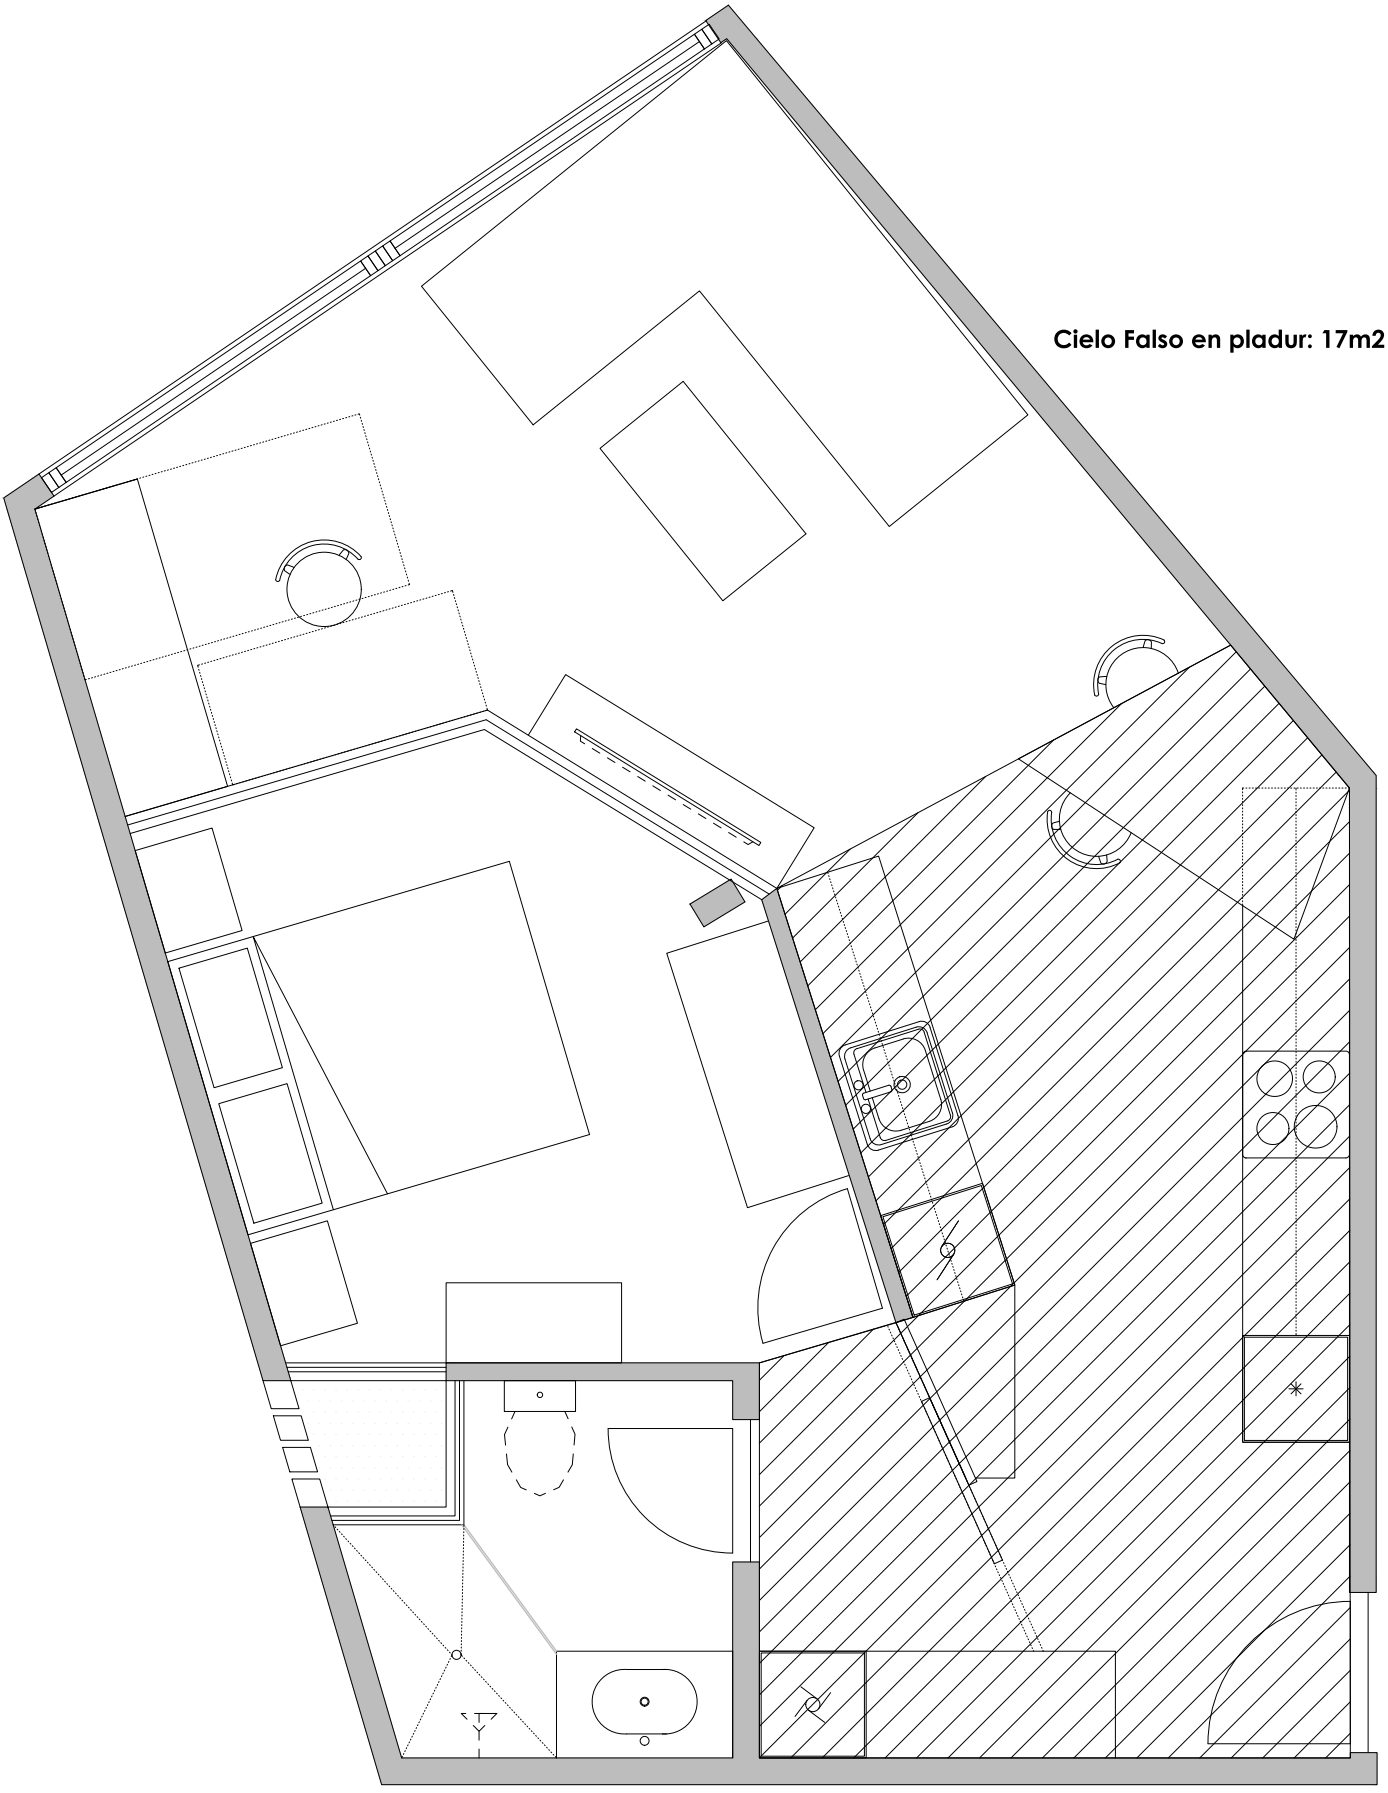


**Cielo Falso en pladur: 17m2**

Valencia 178
Escala 1:30


# 10. Ventana Salon

- Doble vidrio con camara de aire.
- Carpinteria en **aluminio.**
- Color Plata.

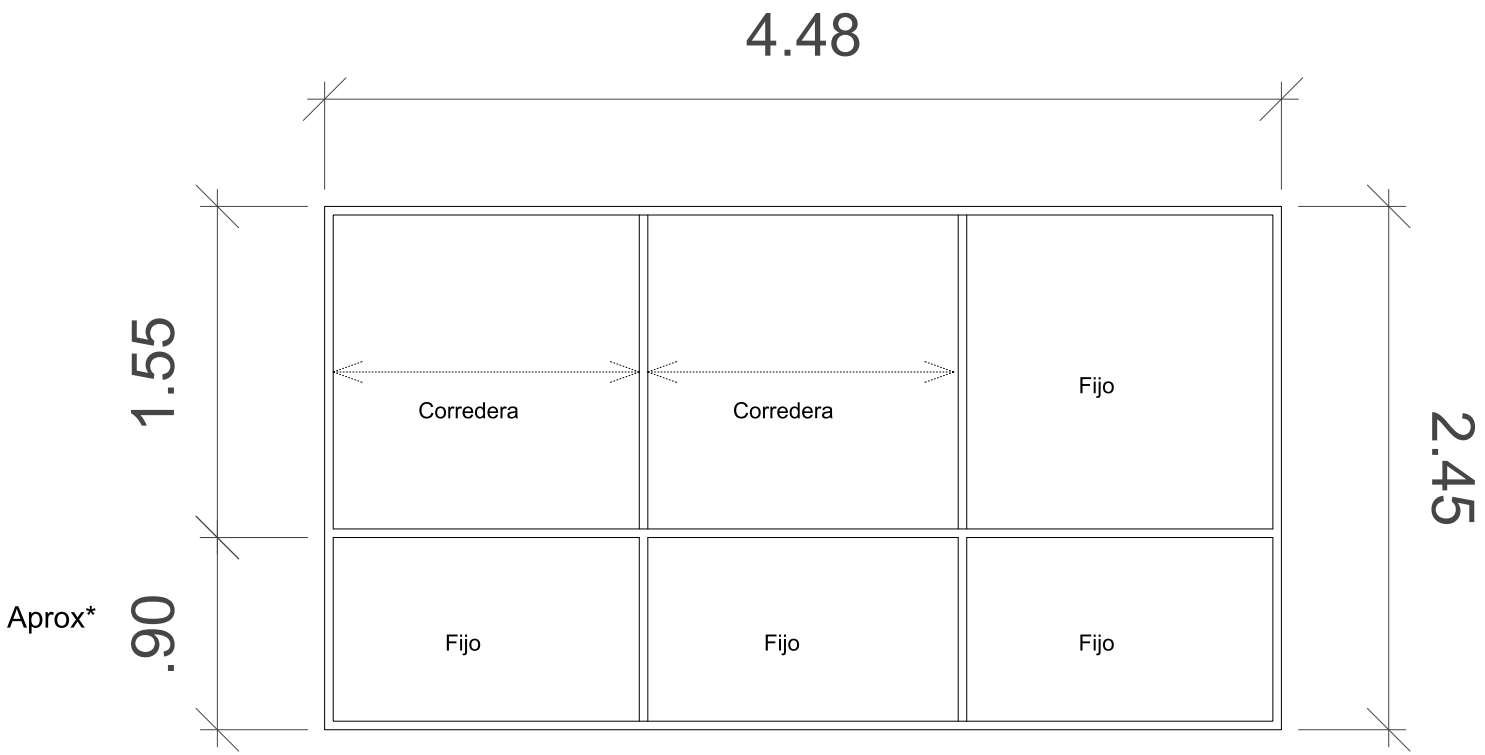


# 10.1 Ventana Habitacion


- Vidrio sencillo.
- Carpinteria lo + sencilla en **aluminio.**
- Color Plata o Negro.

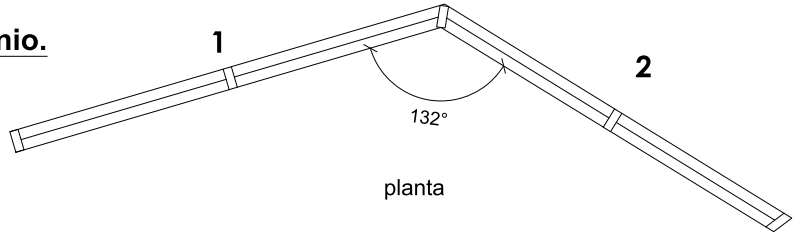


planta

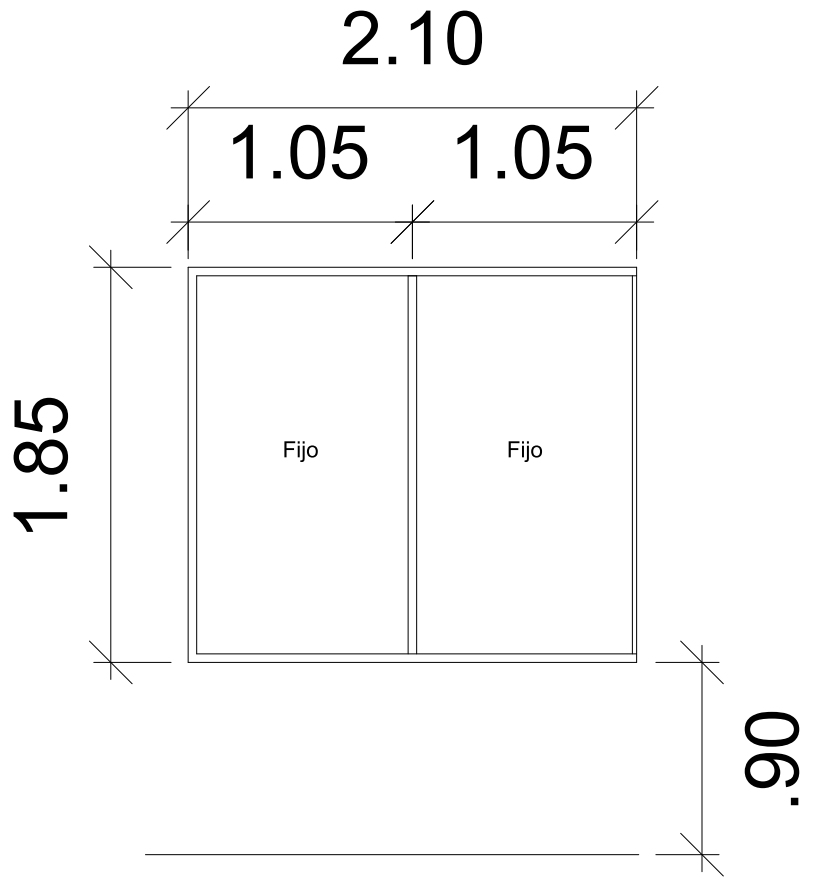


1

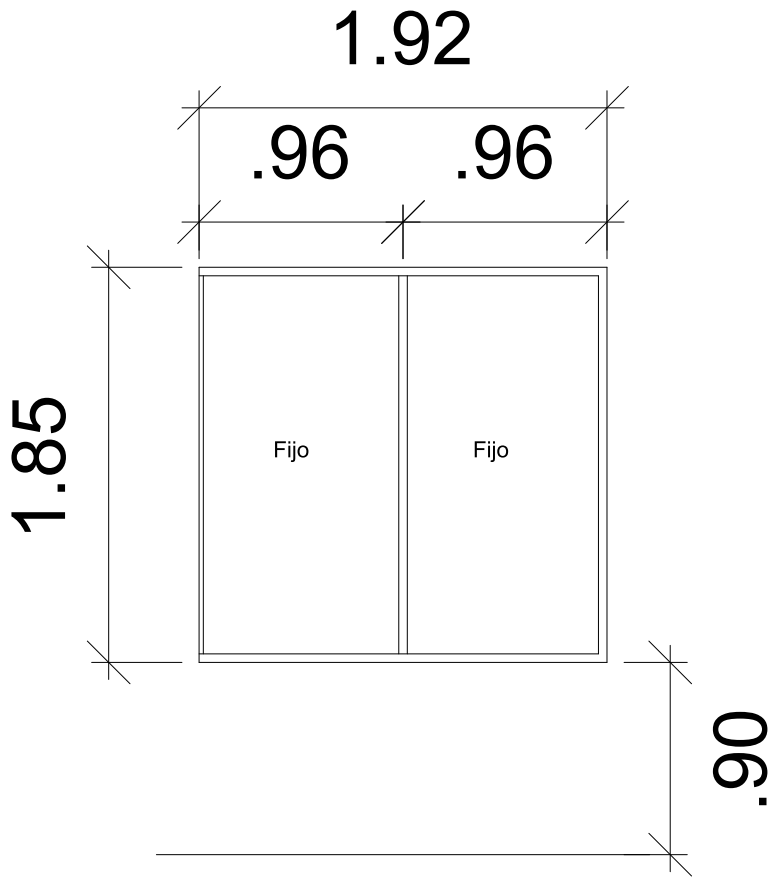


2